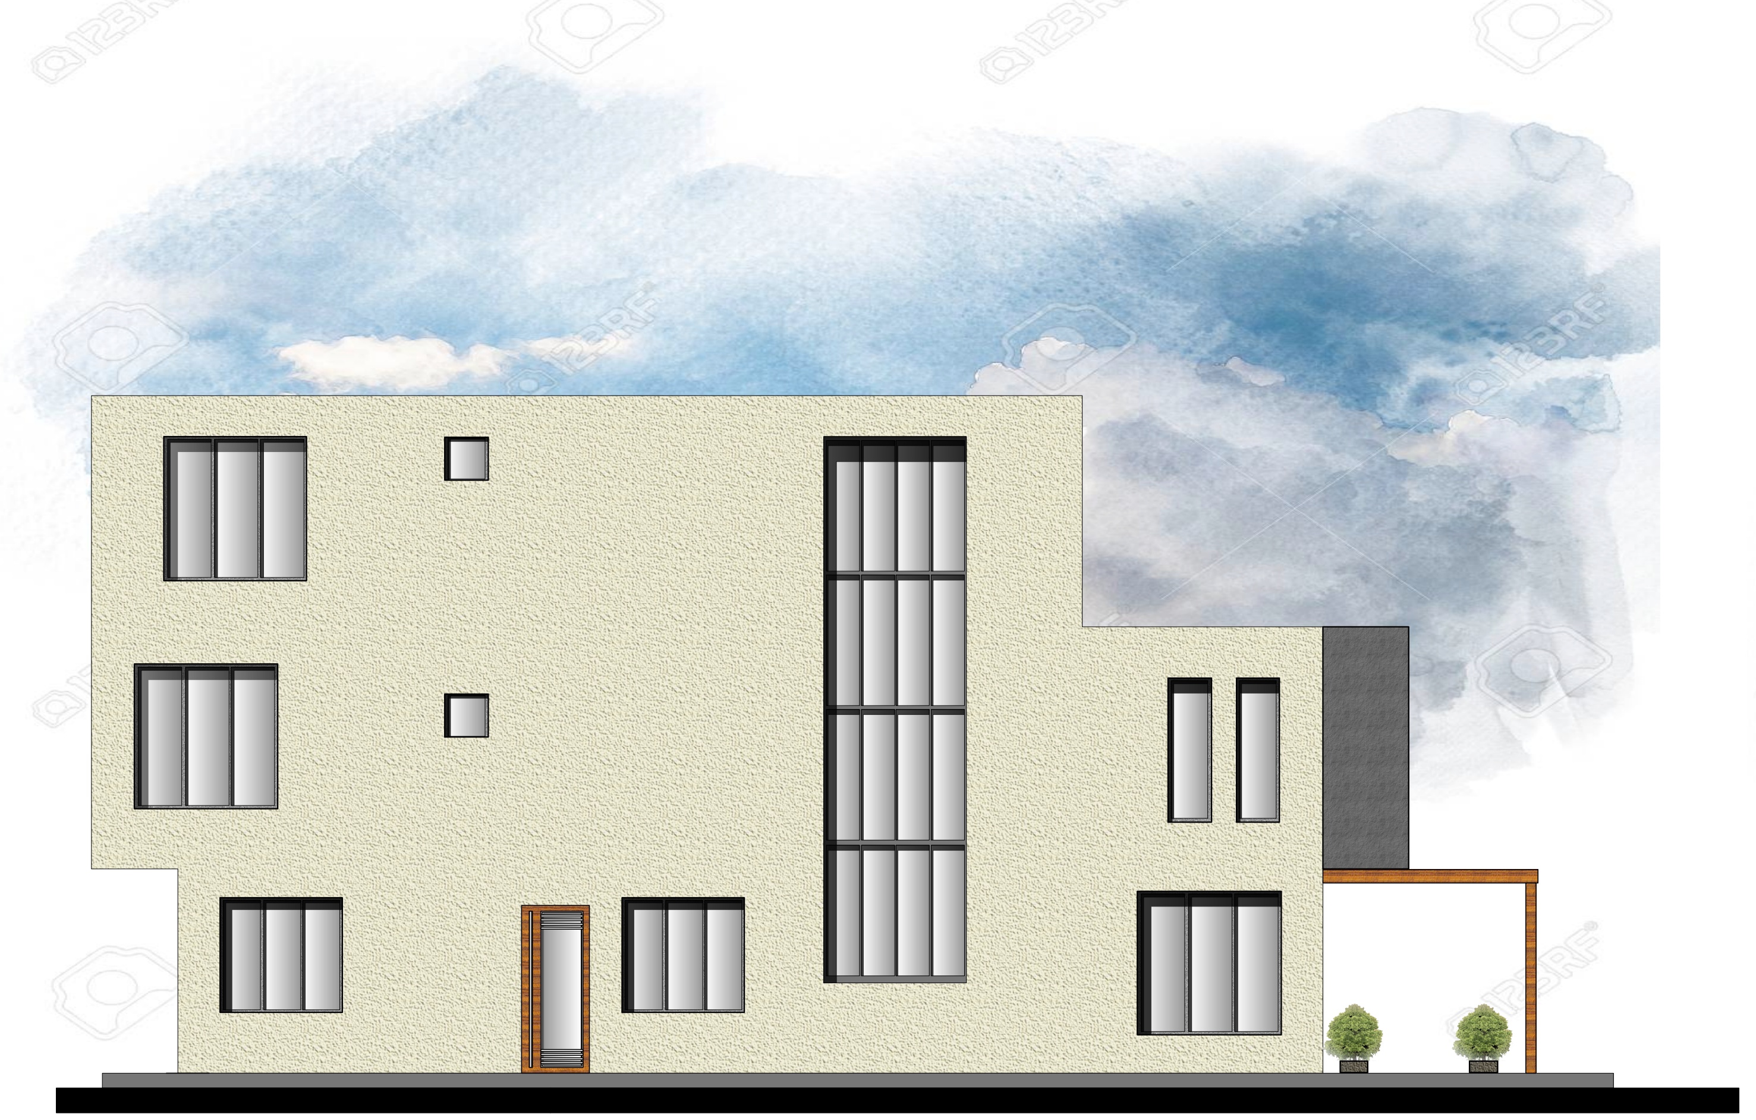

Elevacion Lateral

ESC. 1:100

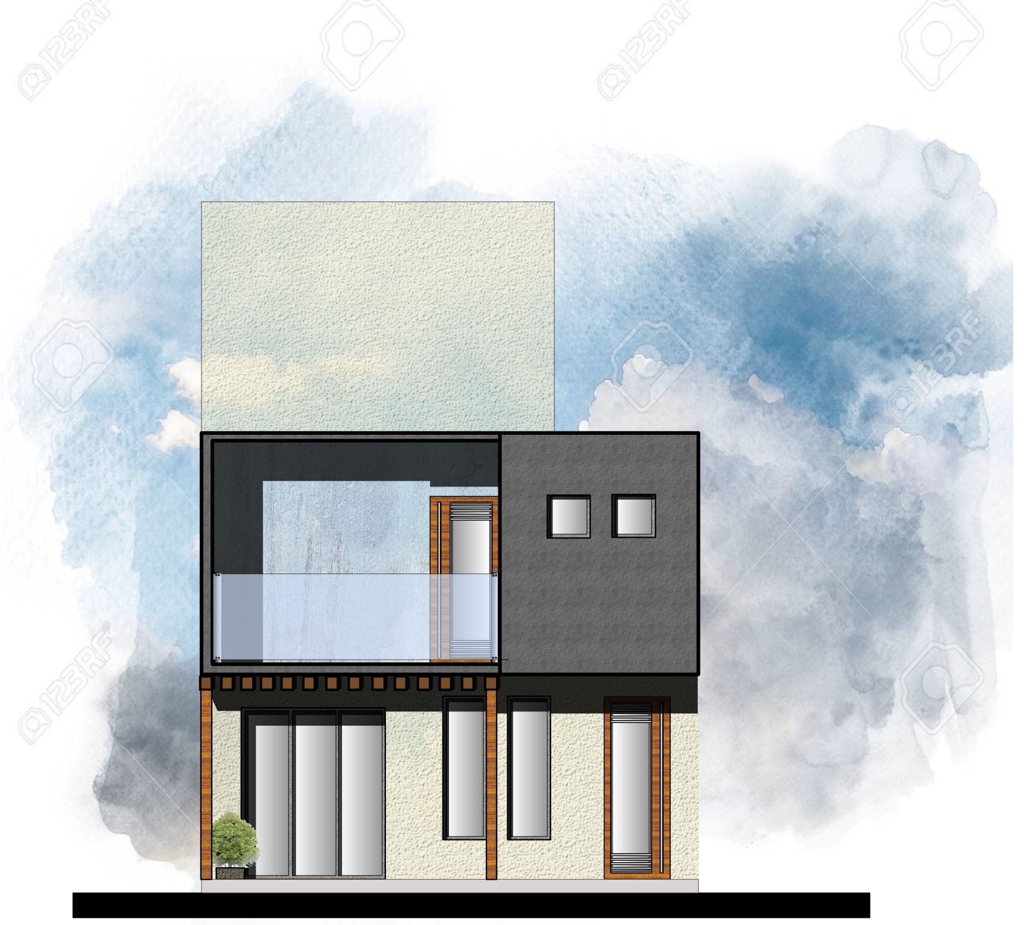

Elevacion Frontal

ESC. 1:100

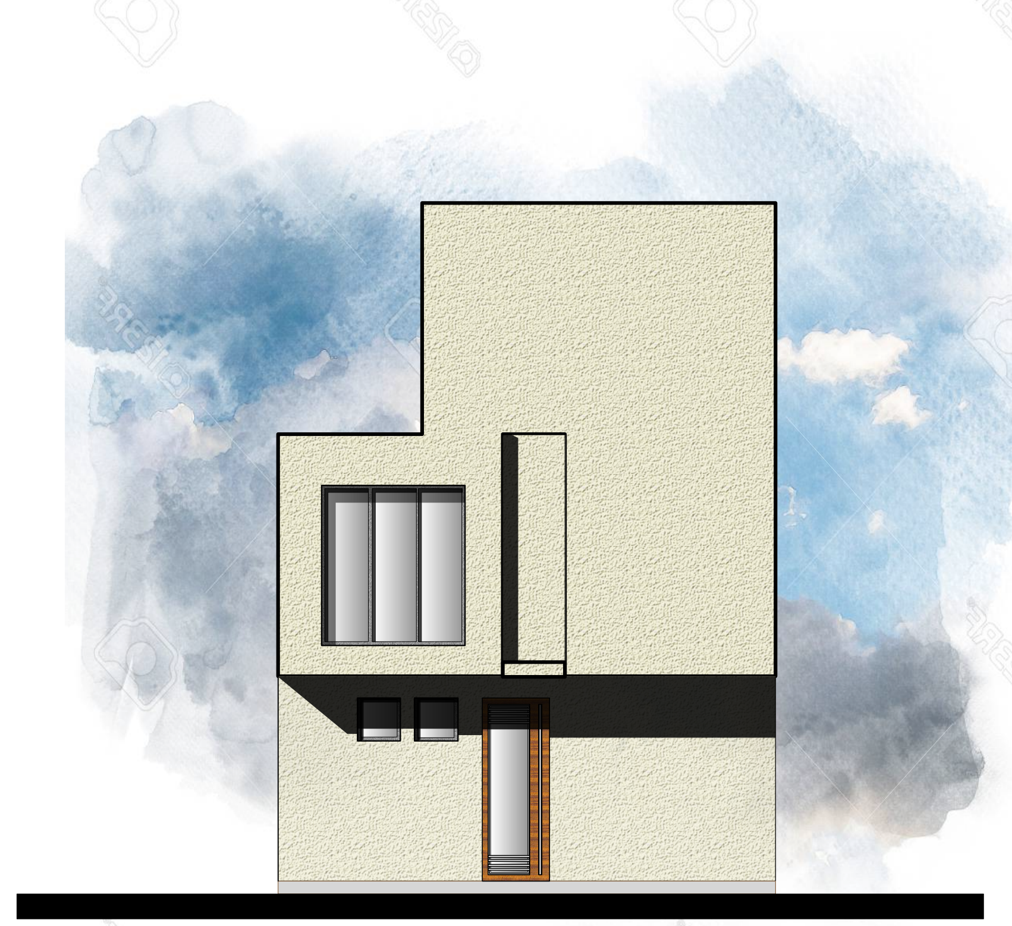

Elevacion Posterior

ESC. 1:100

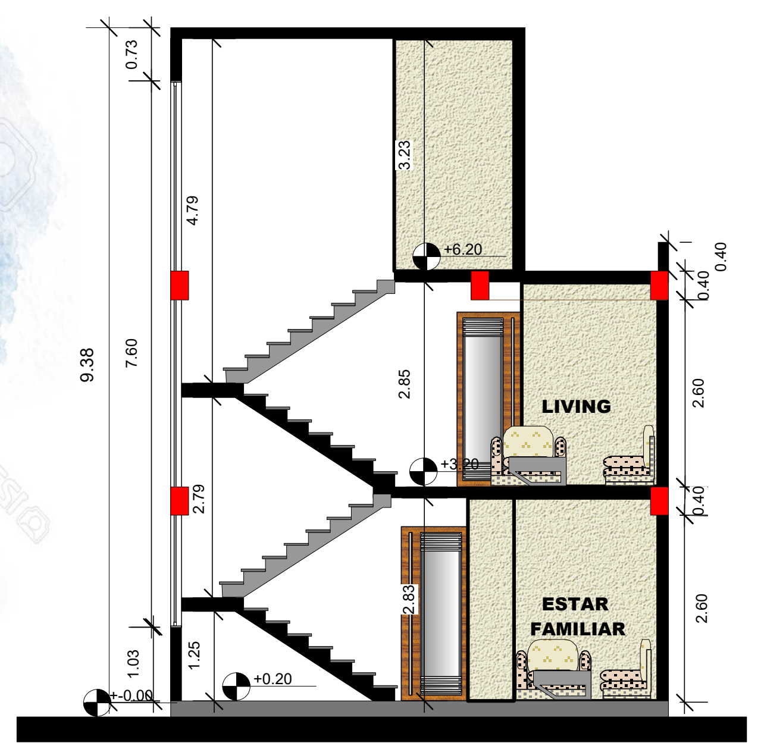

CORTE A - A'

ESC. 1:100

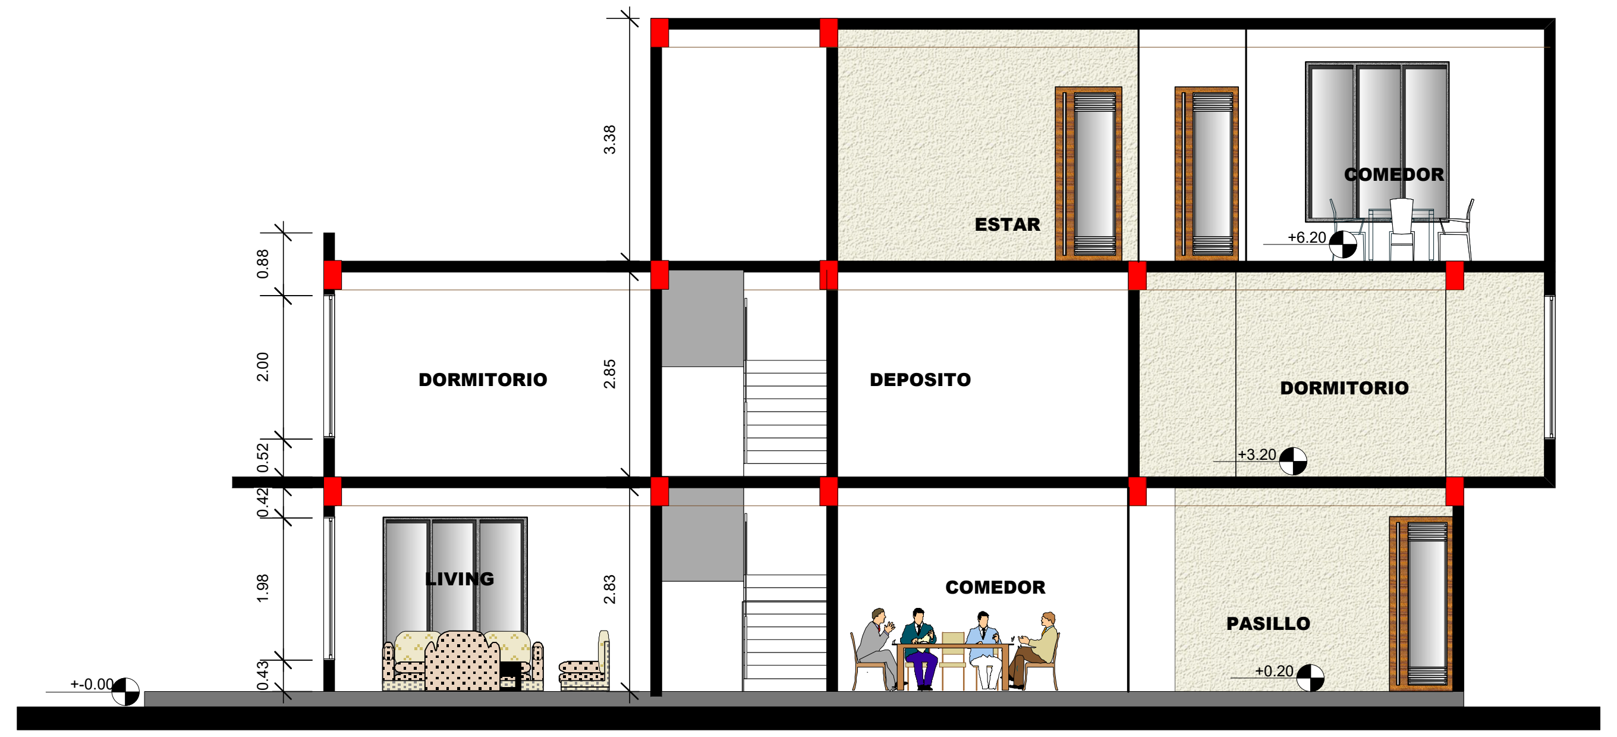

CORTE B - B'

ESC. 1:100

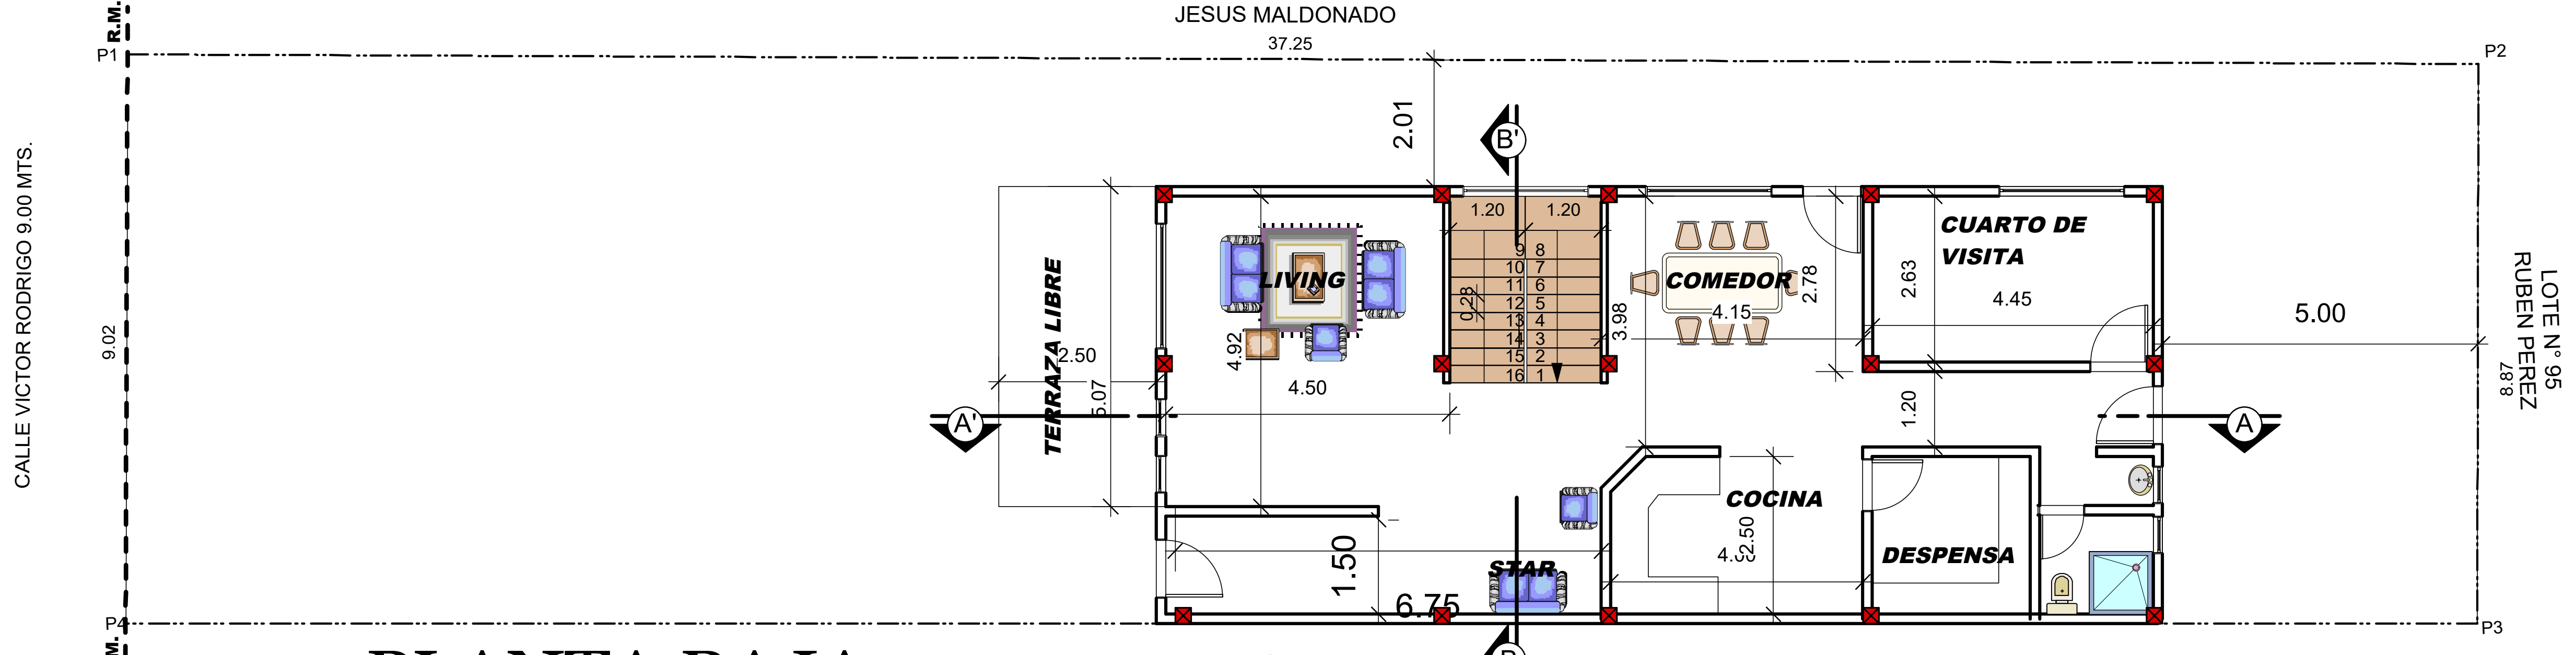

PLANTA BAJA

ESC. 1:100

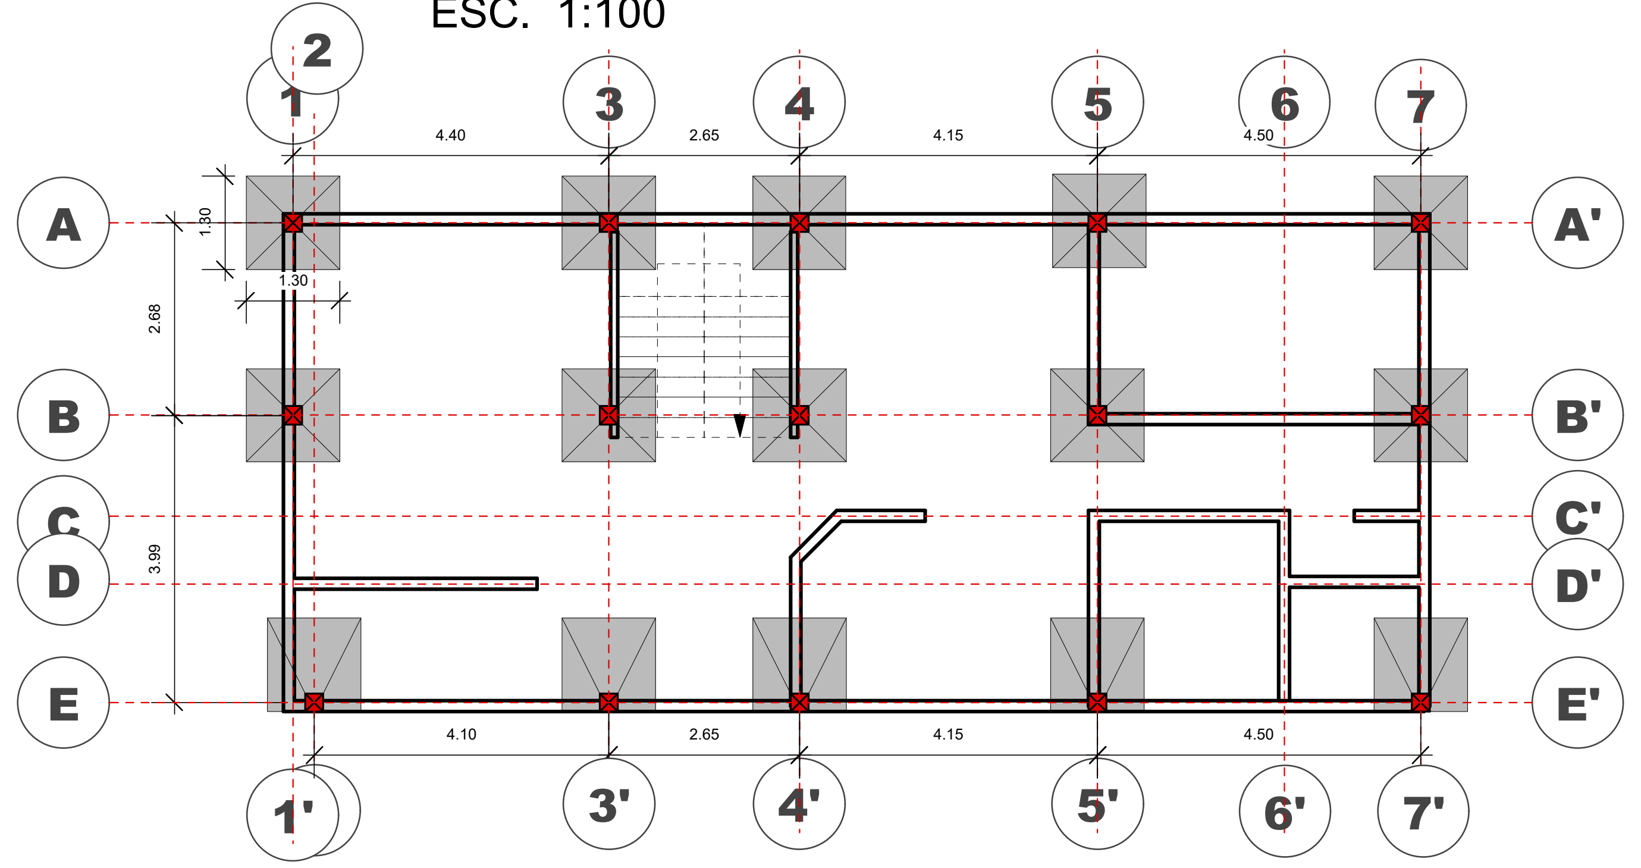

PLANO DE FUNDAIONES

ESC. 1:100

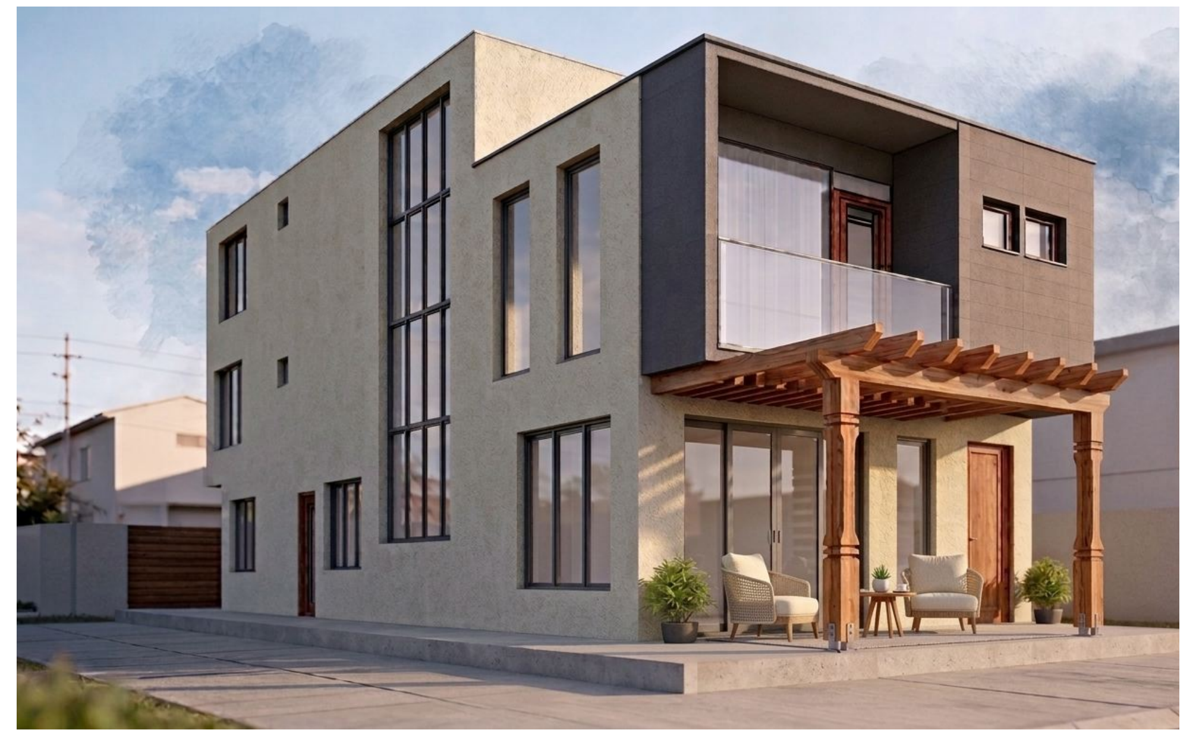

PERSPECTIVA

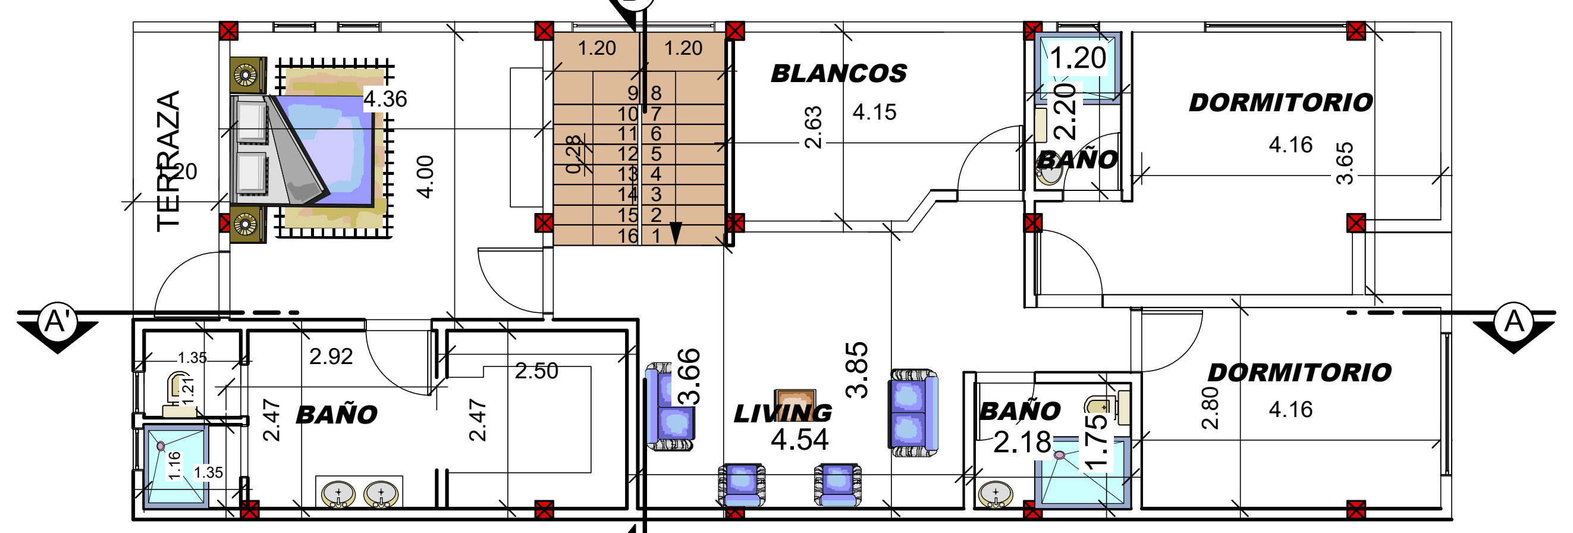

PLANTA 1° PISO

ESC. 1:100

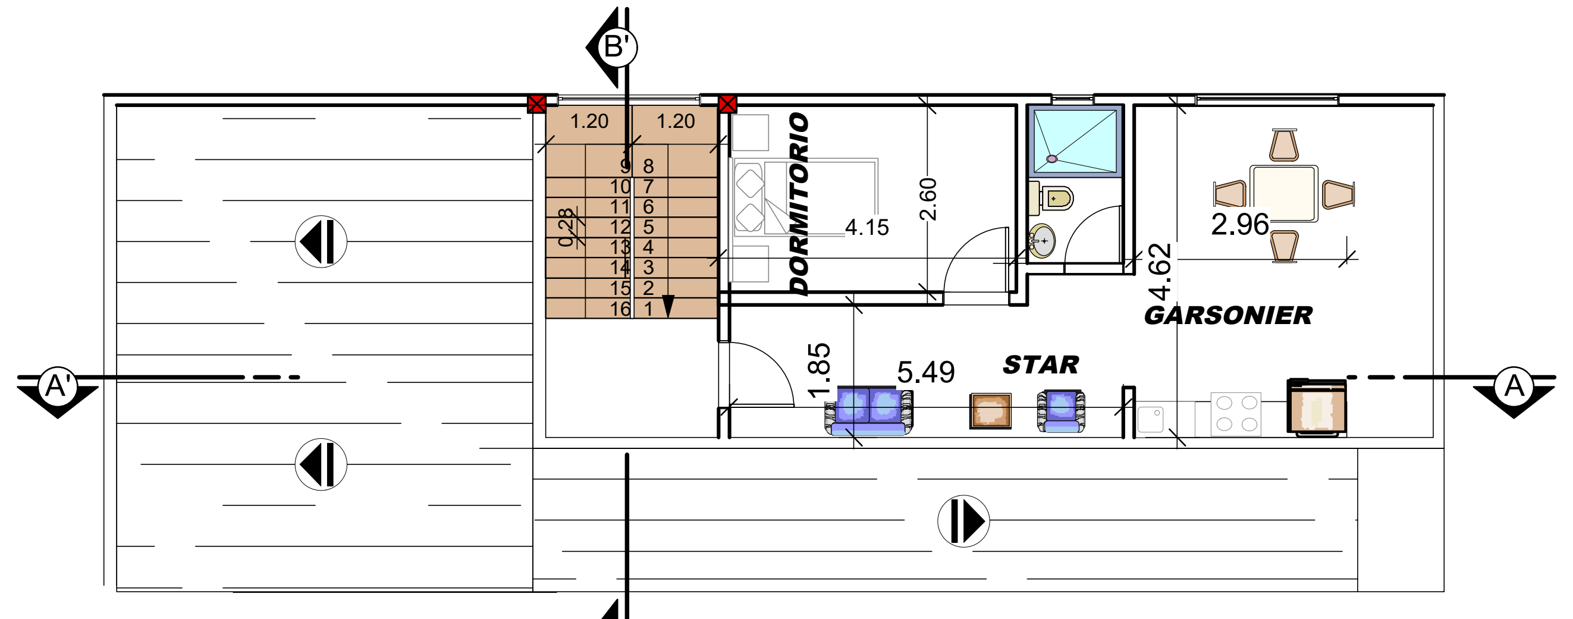

PLANTA ALTILLO

ESC. 1:100

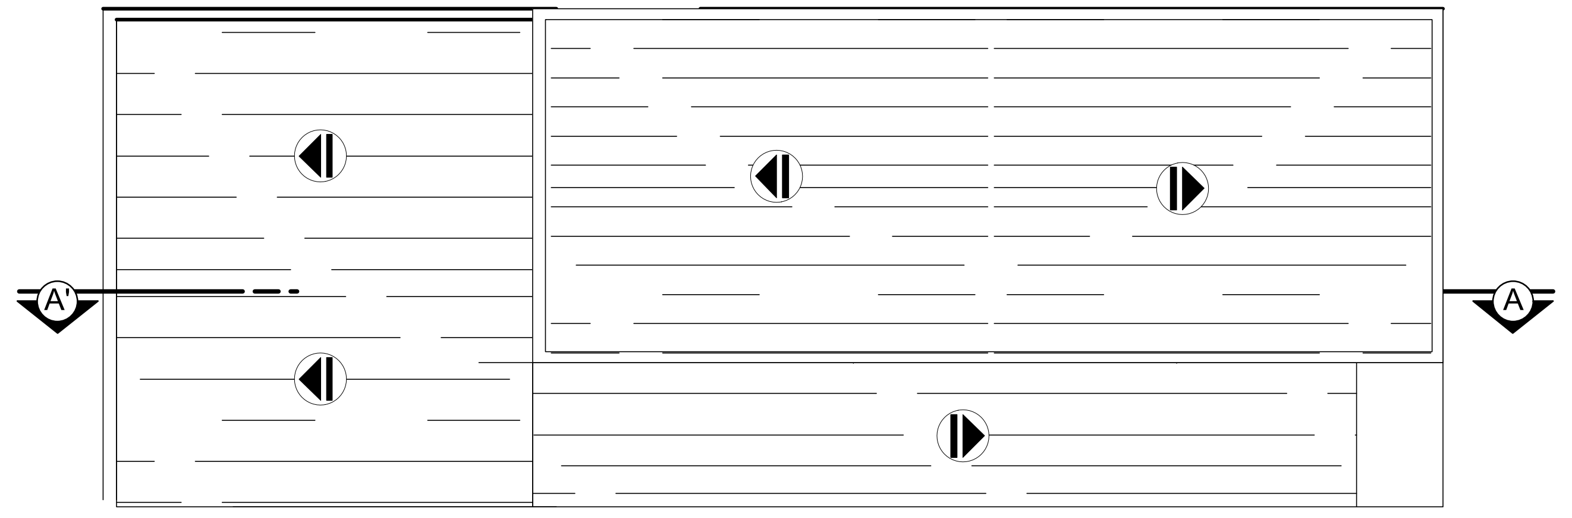

PLANTA CUBIERTA

ESC. 1:100

FICHA DE VEGETACION

PLANTA	ELEVACION	ESPECIE
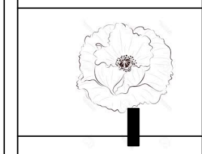	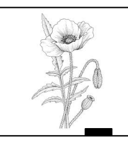	Amapola
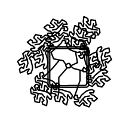		Paraiso
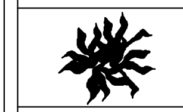		Palmera Enana
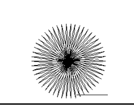	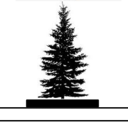	Pino

NOMBRE del PROYECTO y TIPO de EDIF.	DATOS TECNICOS
VIVIENDA UNIFAMILIAR	RELACION DE SUPERFICIES:

RELACION DE SUPERFICIES:

SUP. CONST. PLANTA BAJA	65,66 m2
SUP. CONST. PRIMER PISO	79,27 m2
SUP. CONST. SEGUNDO PISO	53,49 m2
SUP. CONST. TOTAL	198,42 m2

PROPIETARIOS

FIRMA DEL PROPIETARIO (S)

OTROS DATOS

NUMERO DE PLANTAS	3
ALTURA DE LA EDIFICACION	9,38 ml
SUP. LOTE:	340,64 m2
LONG. VERJA:	27,93 ml

SELLO de VISADO o APROBACION

DATOS DE UBICACION

CODIGO CATASTRAL : 05-17-101-063-0-00-000-000
SUBALCALDIA : ALEJO CALATAYUD
DISTRITO : 05
SUB-DISTRITO : 17
ZONA : LACMA
MANZANA : 101
LOTE : 4
CALLE : PASAJE INNOMINADO

PLANO DE UBICACION

N

SELLO de REVALIDACION

ESCALA	LAMINA	FECHA
1:100 1:25	UNICA	FEBRERO DEL 2020

ARQUITECTO RESPONSABLE DEL PROYECTO	REVISION TECNICA	REVISION TECNICA
SELLO C.A.C.		